

DATE OF ISSUE	28.06.18	09.04.21	21.10.25											
DRAWING PACKAGE VERSION	1	2	3											

GENERAL

H8097-G1	SITE SPECIFICATIONS	A	AB	A										
H8097-G2	OVERALL SITE PLAN	A	AB	A										
H8097-G3	SITE LAYOUT AND SETOUT PLAN	A	AB	A										
H8097-G3-1	ANTENNA LAYOUT PLAN	-	-	A										
H8097-G4	SITE ELEVATION	A	AB	A										

ANTENNAS & TRANSMISSION

H8097-A1	eJV ANTENNA SYSTEM CONFIGURATION - SHEET 1 OF 2	A	AB	A										
H8097-A2	eJV ANTENNA SYSTEM CONFIGURATION - SHEET 2 OF 2	-	-	A										
H8097-A3	PHYSICAL ASSET SUMMARY TABLE	-	-	A										
H8097-P1	OPTUS & VODAFONE RF PLUMBING DIAGRAM	A	AB	A										

SHELTER

H8097-F1	EQUIPMENT SHELTER LAYOUT PLAN	A	AB	A										
H8097-F1-1	EQUIPMENT RACK ELEVATION	A	AB	A										

REFERENCE DOCUMENTS

OSD-100	STANDARD CONSTRUCTION NOTES	-	-	C										
OSD-171-1	SITE SIGNAGE TYPICAL GROUND SITE	-	-	B										
OSD-171-3	SIGNAGE LEGEND AND NOTES	-	-	B										
292920_1	POLE CERTIFICATE BY CIVILMART DATED ON 03/09/2025	-	-	0										
16721	GAMCORP FOUNDATION CERTIFICATE DATED 02/09/2025	-	-	0										
SC184419 OPT	SITEPRO 1 STRUCTURAL ANALYSIS AND DESIGN CERTIFICATE DATED ON 15/10/2025	-	-	0										
SP20132-H8097	700mm FACE WIDTH 1000mm OUTRIGGER HEADFRAME SHEET 1 OF 3	-	-	0										
SP20132-H8097	700mm FACE WIDTH 1000mm OUTRIGGER HEADFRAME SHEET 2 OF 3	-	-	0										
SP20132-H8097	700mm FACE WIDTH 1000mm OUTRIGGER HEADFRAME SHEET 3 OF 3	-	-	0										

DISTRIBUTION

OPTUS	SUHAIB OBAID	1	1	1										
CPS TECH	BRETT THOMSON	-	-	1										



OPTUS SITE - H8097

AUSTINS FERRY

JV SITE ID: JH3038

2 PLAN 158154 WAKEHURST ROAD

AUSTINS FERRY

TAS 7011

DRAFT

UPGRADE 5G (eJV)

OPTUS WORK AUTHORITY N° 658102




FOR CONSTRUCTION

Drawing No.
H8097 - 00

2 PLAN 158154 WAKEHURST ROAD
AUSTINS FERRY
TAS 7011

OPTUS SITE H8097
(RFNSA NO: 7011007)

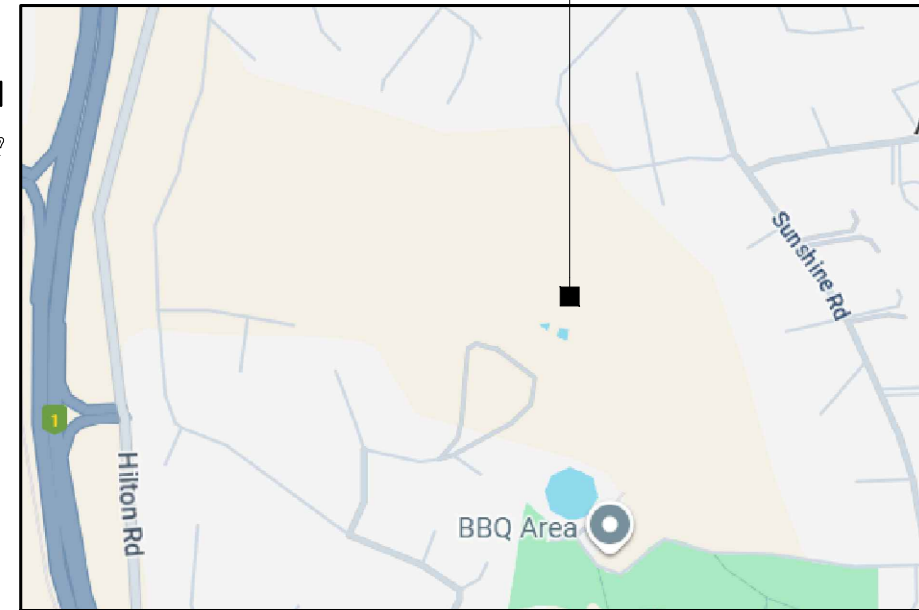

TOPOGRAPHIC MAP ... COPYRIGHT © GOOGLE MAPS

SOURCE: RFNSA	
DATUM: MGA (GDA94)	ZONE: 55
REF LOCATION:	€ MONOPOLE
EASTING	520 051
NORTHING	5 263 789
LATITUDE	-42.77817°
LONGITUDE	147.24512°
WGS84 DATUM (USED BY GOOGLE EARTH® AND GPS DEVICES) CAN BE CONSIDERED SAME AS GDA94 (SOURCE: "GEOCENTRIC DATUM OF AUSTRALIA TECHNICAL MANUAL" VERSION 2.3)	

1. EXISTING OPTUS 27m HIGH CONCRETE MONOPOLE (SR3-BM27-585).
2. STRUCTURAL ADEQUACY OF EXISTING MONOPOLE AND ITS FOUNDATION ARE CONFIRMED BY CIVILMART. REFER TO CERT 292920_1 & GAMCORP FOUNDATION CERTIFICATE 16721 DATED 02/09/2025 FOR DETAILS.
3. NEW OPTUS & VODAFONE PANEL ANTENNAS TO BE INSTALLED ON NEW ANTENNA MOUNTS ON NEW COLLAR MOUNT. NEW OPTUS & VODAFONE RRU's TO BE INSTALLED ON NEW COLLAR MOUNT. REFER TO DRGS. SP20132-H8097 FOR DETAILS.
4. STRUCTURAL ADEQUACY OF NEW COLLAR MOUNT AND NEW ANTENNA MOUNT HAS BEEN DESIGNED AND CERTIFIED BY SITE PRO1. REFER TO CERT_SC184419 OPT FOR DETAILS.
5. ANTENNA MAINTENANCE ACCESS ARRANGEMENT IS VIA EWP BY QUALIFIED RIGGER PERSONNEL ONLY.

EXISTING OPTUS ZONECOOL C3 (3.0m x 2.5m) EQUIPMENT SHELTER PAINTED COLORBOND 'PALE EUCALYPT' SUPPORTED ON STRIP FOOTINGS AND PIERS.

THIS SITE IS LINKED TO THE NETWORK VIA RADIO.

1. ENTER POIMENA RESERVE FROM WAKEHURST ROAD AND TRAVEL TO UPPER CARPARK. OPTUS TO DAISY CHAIN LOCK INTO GATE TO GAIN ACCESS TO GATE.
2. TRAVEL UP EXISTING ACCESS TRACK TO TELSTRA FACILITY.
(NOTE: ACCESS TRACK IS ON/NEXT TO FRISBEE GOLF COURSE, CAUTION SHOULD BE TAKEN)

1. EXISTING EME TRANSMITTING ANTENNAS & CABLING.
2. MANUAL HANDLING.
3. WORKING AT HEIGHTS.
4. SLIP, TRIP AND FALLS.
5. ELECTRICAL HAZARDS.
6. EXTREME WEATHER CONDITIONS / LIGHTNING.
7. SUN EXPOSURE.
8. WILDLIFE / INSECTS

1. SITE SIGNAGE SHALL BE IN ACCORDANCE WITH OSD-171-1 (GROUND SITE) AND OSD-171-3 (SIGNAGE LEGEND AND NOTES).
2. REPLACE EXISTING OUTDATED HAZARDOUS VOLTAGE SIGN WITH NEW HAZARDOUS VOLTAGE SIGN ON EXISTING METER BOX OUTSIDE SHELTER.
3. MERCS-5 SIGNAGE TO BE INSTALLED ON BACK OF NEW PANEL ANTENNAS.
4. REPLACE EXISTING OUTDATED SITE ENQUIRY SIGNAGE WITH NEW SITE ENQUIRY ON EXISTING SHELTER DOOR.

REFER TO EME GUIDE (EMEG) FOR LATEST EME EXCLUSION ZONES FOR EXISTING ANTENNAS AT THIS SITE.

ALL WORKS ARE TO BE IN ACCORDANCE WITH THE OPTUS CONSTRUCTION SPECIFICATION (OSD-010), OPTUS EARTHING SPECIFICATION (OSD-020) AND OPTUS SHELTER SPECIFICATION (OSD-040). LATEST EDITION WITH AMENDMENTS AT TIME OF CONSTRUCTION IS TO APPLY.

EXISTING OPTUS 50A THREE PHASE POWER SUPPLY IS SUFFICIENT FOR THE PROPOSED UPGRADE.

ALL NEW EQUIPMENT AND FEEDER CABLING SHOULD BE BONDED TO THE EXISTING EARTH SYSTEM.
ALL WALKWAYS, HANDRAILS AND EXTRANEIOUS METALWORK ASSOCIATED WITH THE OPTUS INSTALLATION ARE
TO BE BONDED TO THE EXISTING EARTH SYSTEM.
FOR DETAILS OF METHODOLOGY, REFER TO OPTUS EARTHING SPECIFICATION, OSD-020 (LATEST EDITION AT TIME OF
CONSTRUCTION IS TO APPLY).

1. BUILD CONTRACTOR TO ESTABLISH FALL ZONE PRIOR TO COMMENCING ANY CONSTRUCTION OR MAINTENANCE INCLUDING ANTENNA IN ORDER TO ADHERE WITH HEALTH AND SAFETY REGULATIONS.
2. THERE MIGHT BE A RISK THAT THE MOUNTS/SUPPORT STRUCTURE FAILING DUE TO LOOSENING OF BOLTS/NUTS OVER TIME INCREASING THE RISK FOR FALLING OBJECTS (E.G. REPLACEMENT OF EQUIPMENT).
3. THERE MIGHT BE A RISK OF BEING CONFRONTED WITH POISONOUS SNAKES AND SPIDERS WHEN ATTENDING A SITE WEAR PROPER PPE GEARS AND APPROPRIATE CARE MUST BE TAKEN.
4. SITE SURROUNDING AREA LOOKS MUD. PLEASE AVOID RAINY SESSION DURING CONSTRUCTION.

A	21.10.25	ISSUED FOR CONSTRUCTION (UPGRADE 5G (eJVI))	ALL TELECOMS	VB	SA		GL		JM
AB	09.04.21	AS BUILT	METASITE	AU	JB		GC		PJ
A	28.06.18	ISSUED FOR CONSTRUCTION (eJV GREENFIELD PROJECT)	METASITE	JM	JB		GC		PJ
Rev	Date	Revision Details	Consultant	CAD	Designer		Verifier		Approver



Client:	
---------	--

Project:

MOBILE NETWORK
AUSTRALIA
SITE No:- H8097
AUSTINS FERRY
2 PLAN 158154 WAKEHURST ROAD

Drawing Title:

SITE SPECIFICATIONS

Drawing Status:


FOR CONSTRUCTION


Drawing No.

Drawing No.
H8097-G1

Revision

A

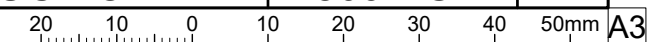

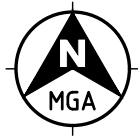

EXISTING/NEW OPTUS/VODAFONE
INSTALLATION. REFER TO DRG.
H8097-G3 FOR DETAILS

EXISTING TELSTRA SITE

PROPOSED EWP SET UP
LOCATION. (REFER TO NOTE 3)

EXISTING TELSTRA 3m
WIDE ACCESS TRACK

EXISTING DIRT ACCESS
TRACK (UPHILL)

EXISTING SITE CONSUMER
MAINS IN U/G CONDUIT

EXISTING FENCE LINE (TYP.)

EXISTING TREE (TYP.)

EXISTING WATER RESERVOIR

EXISTING PUMP BUILDING

EXISTING 3 PHASE POWER SUPPLY
POLE WITH TRANSFORMER #100544
(SITE POINT OF SUPPLY)

NOTES:

1. ALL INFORMATION TO BE CHECKED ON SITE PRIOR TO FABRICATION AND CONSTRUCTION.
2. DRAWINGS BASED ON INFORMATION PROVIDED BY OTHERS.
3. CONSTRUCTION CONTRACTOR TO CONFIRM SUITABILITY OF PROPOSED EWP SET-UP/PARKING LOCATION ON SITE PRIOR TO WORK COMMENCING.
4. SERVICES INFORMATION CONTAINED ON THIS DRAWING IS INDICATIVE ONLY AND REFERENCE SHOULD BE MADE TO THE AUTHORITIES DRAWINGS TO CONFIRM ACCURACY AND COMPLETENESS. WHERE INFORMATION IS AVAILABLE, THE SUB-SURFACE SERVICES INSTALLED BY AGENTS OTHER THAN AUTHORITIES HAVE BEEN SHOWN, BUT ADDITIONAL UNDOCUMENTED SERVICES MAY BE PRESENT. SHOULD THE CONTRACTOR BELIEVE THAT SUB-SURFACE SERVICES ARE AT RISK OF DAMAGE DURING CONSTRUCTION, THE CONTRACTOR SHOULD NOTIFY THE RELEVANT AUTHORITIES AND ESTABLISH THE EXACT LOCATION OF THE SERVICES.

LEGEND

- E ——— E ——— EXISTING O/H POWER SUPPLY
- e ——— e ——— EXISTING U/G CONSUMER MAINS
- / ——— / ——— EXISTING FENCE LINE

OVERALL SITE PLAN

SCALE 1:2000

Rev	Date	Revision Details	Consultant	CAD	Designer	Verifier	Approver
A	21.10.25	ISSUED FOR CONSTRUCTION (UPGRADE 5G (eJV))	ALL TELECOMS	VB	SA	GL	JM
AB	09.04.21	AS BUILT	METASITE	AU	JB	GC	PJ
A	28.06.18	ISSUED FOR CONSTRUCTION (eJV GREENFIELD PROJECT)	METASITE	JM	JB	GC	PJ

Client:

OPTUS

Project:

MOBILE NETWORK
AUSTRALIA
SITE No:- H8097
AUSTINS FERRY
2 PLAN 158154 WAKEHURST ROAD

Drawing Title:

OVERALL SITE PLAN

Drawing Status:

FOR CONSTRUCTION

Drawing No.

H8097-G2

Revision

A



EXISTING OPTUS 2.4m HIGH CHAINWIRE SECURITY FENCE WITH 1.5m WIDE SINGLE ACCESS GATE

EXISTING OPTUS 75mm THICK SINGLE SIZE GRAVEL/RECYCLED CONCRETE OVER WEED MAT WITH TIMBER EDGING

EXISTING OPTUS 200mm HIGH TIMBER STEPS

INSTALL NEW VODAFONE NOKIA A YGE GPS ANTENNA (1 OFF) ON THE TOP OF SHELTER WALL. ENSURE MIN. 500mm HORIZONTAL SEPERATION FROM OTHER GPS ANTENNA

EXISTING OPTUS ZONECOOL C3 EQUIPMENT SHELTER TO BE RECONFIGURED TO ACCOMMODATE EXISTING & PROPOSED EQUIPMENTS. REFER TO DRG. H8097-F1 FOR DETAILS

REPLACE EXISTING OPTUS GPS ANTENNA (1 OFF) WITH NEW OPTUS ERICSSON GNSS GPS ANTENNA (1 OFF) ON THE TOP OF SHELTER WALL

REPLACE EXISTING OUTDATED HAZARDOUS VOLTAGE SIGN WITH NEW HAZARDOUS VOLTAGE SIGN ON EXISTING METER BOX OUTSIDE SHELTER

EXISTING OPTUS HDPE ELECTRICAL DRAW PIT

REPLACE EXISTING OUTDATED SITE ENQUIRY SIGNAGE WITH NEW SITE ENQUIRY ON EXISTING SHELTER DOOR

EXISTING OPTUS 1.5m WIDE SINGLE ACCESS GATE

EXISTING TELSTRA SUB-MAINS FROM SITE GROUP METER

EXISTING SITE GROUP METER BOX ON FREE STANDING "H" FRAME TO HOST OPTUS METER AND TELSTRA ONE WITH ACCESSORIES

EXISTING SITE CONSUMER MAINS IN U/G CONDUIT. APPROX. 260m

EXISTING OPTUS SITE ACCESS ROUTE

REUSE EXISTING OPTUS H&S 9/18 HYBRID CABLE (1 OFF) (LENGTH: 40m) AND SHARED H&S 9/18 HYBRID CABLE (1 OFF) (LENGTH: 40m) TO BE ALLOCATED TO OPTUS TO RUN IN EXISTING OPTUS 450mm WIDE CABLE LADDER

REUSE EXISTING VODAFONE H&S 9/18 HYBRID CABLE (1 OFF) (LENGTH: 40m) AND INSTALL NEW H&S 9/18 (10mm²) HYBRID CABLES (1 OFF) (LENGTH: 40m) FOR VODAFONE TO RUN IN EXISTING OPTUS 450mm WIDE CABLE LADDER

EXISTING TELSTRA FENCE CUT LOCALLY FOR OPTUS CABLE LADDER TO PASS THROUGH

NOTES:

1. ALL ANTENNA ORIENTATIONS ARE IN DEGREE RELATIVE TO TRUE NORTH.
2. REFER TO DRG. H8097-G1 FOR SITE SPECIFICATION NOTES.
3. REFER TO DRG. H8097-A1 TO A3 FOR ANTENNA SYSTEM CONFIGURATIONS.
4. ALL ANCILLARIES TO BE INSTALLED BEHIND ANTENNAS ON NEW MOUNTING POLE.
5. EXISTING CORRODED, DAMAGED OR MISSING ANTENNA MOUNT U-BOLTS AND FIXING TO BE REPLACED AS REQUIRED.

LEGEND

- 0 e — 0 e — EXISTING OPTUS U/G SUBMAIN CABLE
- T e — T e — EXISTING TELSTRA U/G POWER SUPPLY
- / — / — EXISTING FENCE LINE
- e — e — EXISTING U/G CONSUMER MAINS

ANTENNA LEGEND



NEW, REPLACE

DRAFT

EXISTING OPTUS 27m HIGH CONCRETE MONOPOLE (SR3-BM27-585)

MGA ZONE	55
E	520 051
N	5 263 789
AT	€ MONOPOLE

EXISTING TELSTRA COMPOUND FENCE

EXISTING TELSTRA EQUIPMENT SHELTER

DETAIL SCALE 1:100

Rev	Date	Revision Details	Consultant	CAD	Designer	Verifier	Approver
A	21.10.25	ISSUED FOR CONSTRUCTION (UPGRADE 5G (eJV))	ALL TELECOMS	VB	SA	GL	JM
AB	09.04.21	AS BUILT	METASITE	AU	JB	GC	PJ
A	28.06.18	ISSUED FOR CONSTRUCTION (eJV GREENFIELD PROJECT)	METASITE	JM	JB	GC	PJ



Client:

Project:

MOBILE NETWORK AUSTRALIA
SITE No:- H8097
AUSTINS FERRY
2 PLAN 158154 WAKEHURST ROAD

Drawing Title:

SITE LAYOUT AND SETOUT PLAN

Drawing Status:


FOR CONSTRUCTION

Drawing No.

H8097-G3

Revision

A

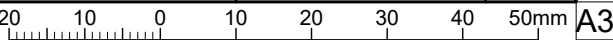



REMOVE EXISTING VODAFONE HUAWEI RRU3952 (L850) (3 OFF), RRU3953 (U9) (3 OFF), RRU3971 (L18) (3 OFF) & RRU3971 (L21) (3 OFF). INSTALL NEW VODAFONE NOKIA RRU AHPB (L7) (1 OFF PER SECTOR, 3 OFF TOTAL), AHCA (L8.5) (1 OFF PER SECTOR, 3 OFF TOTAL) AND AHEGG (L18/L21) (2 OFF PER SECTOR, 6 OFF TOTAL) ON NEW RRU MOUNT CONNECTED TO NEW COLLAR MOUNT

REMOVE EXISTING OPTUS HUAWEI RRU3262 (L7) (3 OFF), RRU3936 (U9) (3 OFF), RRU3971 (L18) (3 OFF), RRU3971 (L21) (3 OFF) & RRU3281 (L26) (3 OFF). INSTALL NEW OPTUS ERICSSON RRU4480 (L7/NL9) (1 OFF PER SECTOR, 3 OFF TOTAL), RRU4466 (L18/NL21/L26) (1 OFF PER SECTOR, 3 OFF TOTAL) AND FUTURE RRU (2 OFF PER SECTOR, 6 OFF TOTAL) ON NEW RRU MOUNT CONNECTED TO NEW COLLAR MOUNT

REPLACE EXISTING eJV 12P HUAWEI ASI4517R1 PANEL ANTENNAS (3 OFF) WITH NEW eJV 16P COMMScope RRV2VV-6533D-R8 PANEL ANTENNAS (1 OFF PER SECTOR) (FOR SECTOR 11-J, 21-J, & 31-J) ON NEW ANTENNA MOUNT CONNECTED TO NEW COLLAR MOUNT

REMOVE EXISTING VODAFONE COMBINERS COM2 (E12F03P18) (3 OFF) & COM4 (E14F05P17) (6 OFF). INSTALL NEW VODAFONE COMBINER COM2g (E14F06P81) (1 OFF PER SECTOR, 3 OFF TOTAL) BEHIND NEW PANEL ANTENNAS ON NEW MOUNT

INSTALL NEW OPTUS ERICSSON AIR3268 B78Y (NR35) ANTENNAS (1 OFF PER SECTOR) (FOR SECTOR 12-0, 22-0, & 32-0) ON NEW ANTENNA MOUNT CONNECTED TO NEW COLLAR MOUNT

INSTALL NEW VODAFONE NOKIA AVQL (NR36) ANTENNAS (1 OFF PER SECTOR) (FOR SECTOR 13-V, 23-V, & 33-V) (BELOW OPTUS AAU) ON NEW ANTENNA MOUNT CONNECTED TO NEW COLLAR MOUNT

REPLACE EXISTING COLLAR MOUNT WITH NEW COLLAR MOUNT. REFER TO DRGS. SP20132-H8097 FOR DETAILS

EXISTING OPTUS 27m HIGH CONCRETE MONOPOLE (SR3-BM27-585)

NOTES:

1. ALL ANTENNA ORIENTATIONS ARE IN DEGREE RELATIVE TO TRUE NORTH.
2. REFER TO DRG. H8097-G1 FOR SITE SPECIFICATION NOTES.
3. REFER TO DRG. H8097-A1 TO A3 FOR ANTENNA SYSTEM CONFIGURATIONS.
4. EXISTING CORRODED, DAMAGED OR MISSING ANTENNA MOUNT U-BOLTS AND FIXING TO BE REPLACED AS REQUIRED.
5. CORROSION HAS BEEN IDENTIFIED ON THE EXISTING THREADED RODS/BOLTS ON THE STRAP MOUNT WHICH NEED TO BE CLEANED AND RE-GALVANIZED OR REPLACED WITH NEW BOLTS IF REQUIRED.

DRAFT

REMOVE EXISTING OPTUS COMBINERS COM2a (E12F13P25) (3 OFF) & COM3 (E16V90P56) (6 OFF). INSTALL NEW OPTUS REJ FILTER (E14V00P21) (1 OFF PER SECTOR, 3 OFF TOTAL) BEHIND NEW PANEL ANTENNAS ON NEW MOUNT

EXISTING OPTUS ϕ 600 PARABOLIC ANTENNA (1 OFF)

ANTENNA LAYOUT PLAN @23.10m

DETAIL
SCALE 1:20

2
G3

ANTENNA LEGEND



Client:

Project:

MOBILE NETWORK
AUSTRALIA
SITE No:- H8097
AUSTINS FERRY
2 PLAN 158154 WAKEHURST ROAD

Drawing Title:

ANTENNA LAYOUT PLAN

Drawing Status:

FOR CONSTRUCTION

Drawing No.

H8097-G3-1

Revision

A


Rev	Date	Revision Details	Consultant	CAD	Designer	Verifier	Approver
A	21.10.25	ISSUED FOR CONSTRUCTION (UPGRADE 5G (eJV))	ALL TELECOMS	VB	SA	GL	JM

ANTENNA DETAILS	
PHYSICAL ANTENNA GROUP (N2)	
CO-ORDINATES (N5)	LATITUDE
	LONGITUDE
ANTENNA OPERATOR	
PHYSICAL ANTENNA NUMBER (N3)	
PHYSICAL ANTENNA ID (N4)	
ANTENNA ALIAS	
ANTENNA STATUS	
PHYSICAL AZIMUTH (°) (N6)	
PHYSICAL ANT CL EL (m) (N7)	
MECH DOWN-TILT (°)	
MODEL NO.	
MANUFACTURER	
TYPE	
NO. OF RF PORTS / TxRx	
PORT TYPE	
BAND CAPABILITY	
DIMENSIONS (HxWxD) (mm)	
WEIGHT (kg)	
RF SECTOR & BAND ALLOCATION	
RF SECTOR ID / SUB-SECTOR ID	
PHYSICAL ARRAY ID	
LOGICAL ANTENNA PORT	
PHYSICAL ANTENNA PORT (OEM LABEL)	
ETILT (N8)	
ARRAY BEAM OFFSET (°)	
ARRAY BEAM AZIMUTH (°)	
ARRAY BAND CAPABILITY	
ASSIGNED ARRAY OPERATOR	
ASSIGNED RF PORT FREQUENCY 1	
ASSIGNED RF PORT FREQUENCY 2	
ASSIGNED RF PORT FREQUENCY 3	
ASSIGNED RF PORT FREQUENCY 4	

1. THIS ANTENNA TABLE SHALL BE READ IN CONJUNCTION WITH THE DETAIL RF PLUMBING DRAWING FOR THIS SITE.
2. A PHYSICAL SECTOR GROUP IS DEFINED AS A GROUP OF ANTENNAS GENERALLY ORIENTATED WITH SIMILAR AZIMUTHS AND EACH GROUP IS ASSIGNED A NUMBER 1, 2, 3, 4, ETC. THE PHYSICAL SECTOR GROUP MAY INCLUDE SINGLE BEAM OR MULTI-BEAM ANTENNAS. IN THE CASE OF MULTI-BEAM ANTENNAS THE RF SECTOR MAY DIFFER TO THE PHYSICAL SECTOR.
3. THE PHYSICAL ANTENNA NUMBER IS DEFINED BY ASSIGNING SEQUENCED NUMBERS TO EACH JV OPERATOR'S ANTENNAS WITHIN A PHYSICAL SECTOR GROUP, STARTING FROM LEFT TO RIGHT, TOP TO BOTTOM.
4. THE PHYSICAL ANTENNA ID IS DEFINED BY THE NUMBER MADE UP BY CONCATENATING THE PHYSICAL SECTOR GROUP NUMBER WITH THE PHYSICAL ANTENNA NUMBER & THE FIRST LETTER FROM THE OPERATOR'S NAME OR JOINT (O, V, J), SAME AS THE SAO NUMBER, AS SPECIFIED IN OSD-070 SECTION 5.6.
5. ANTENNA CO-ORDINATES ARE TO BE IN GDA94/GDA2020 REFERENCE SYSTEM, SPECIFIED FOR CENTRE OF EACH SECTOR TO NEAREST METRE.
6. THE PHYSICAL AZIMUTH (°) IS DEFINED AS THE DIRECTION OF THE PHYSICAL ANTENNA BORE SIGHT WITH RESPECT TO TRUE NORTH. AZIMUTHS OF EACH BEAM OF MULTI-BEAM ANTENNAS ARE NOT DOCUMENTED IN THIS TABLE.
7. THE PHYSICAL ANT CL EL (m) IS DEFINED AS THE MID-HEIGHT OF THE PHYSICAL ANTENNA. THE HEIGHT OF INDIVIDUAL BEAMS OR DIFFERENT SEGMENTS OF MULTI-BEAM OR HYBRID ANTENNAS (IPAA) ARE NOT DOCUMENTED IN THIS TABLE.
8. ELECTRICAL DOWN-TILTS ARE ONLY ACCURATE AT TIME OF BUILD AS THEY ARE FREQUENTLY OPTIMISED. ALWAYS REFER TO CURRENT VALUES IN MNIS.

DRAFT

	</
--	--	----

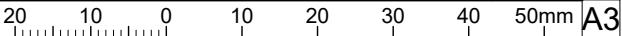

PHYSICAL ASSET SUMMARY TABLE

[illegible][illegible]

COAXIAL FEEDER / HFDC TRUNK CABLES							
CABLE ALIAS	STATUS	LENGTH (m)	OPERATOR	PHY ANT GRP	QTY	COAX BAND ASIGNMENT	MFR
HFDC 9/18 C10	EXISTING	40	O	1	2	LBHB	H+S
HFDC 9/18 C10	EXISTING	40	V	1	1	LBHB	H+S
HFDC 9/18 C10	NEW	40	V	1	1	LBHB	H+S

NOTES:


1. THIS DRAWING SHALL BE READ IN CONJUNCTION WITH RF PLUMBING DRAWING H8097-P1.
2. INFORMATION IN THE TABLES SUPPLIED AND VERIFIED BY OPTUS.
3. ANCILLARIES REFER TO ITEMS AT OR NEAR THE ANTENNA.
4. ALL RF TAILS NOT TO BE MORE THAN 5m.
5. TRUNK LENGTH ARE ESTIMATED, ROUNDED UP TO THE NEXT 10m.

									Client: 	Project: MOBILE NETWORK AUSTRALIA SITE No:- H8097 AUSTINS FERRY 2 PLAN 158154 WAKEHURST ROAD	Drawing Title: PHYSICAL ASSET SUMMARY TABLE			
A 21.10.25 ISSUED FOR CONSTRUCTION (UPGRADE 5G (eJV)) ALL TELECOMS VB SA GL JM											Drawing Status: FOR CONSTRUCTION		Drawing No. H8097-A3	Revision A
Rev	Date	Revision Details			Consultant	CAD	Designer				Verifier	Approver		

Copyright © Optus Mobile Pty Ltd ABN 65 054 365 696. ALL RIGHTS RESERVED. VERSION 2.0 NOVEMBER 2013

201001020304050mm

A3

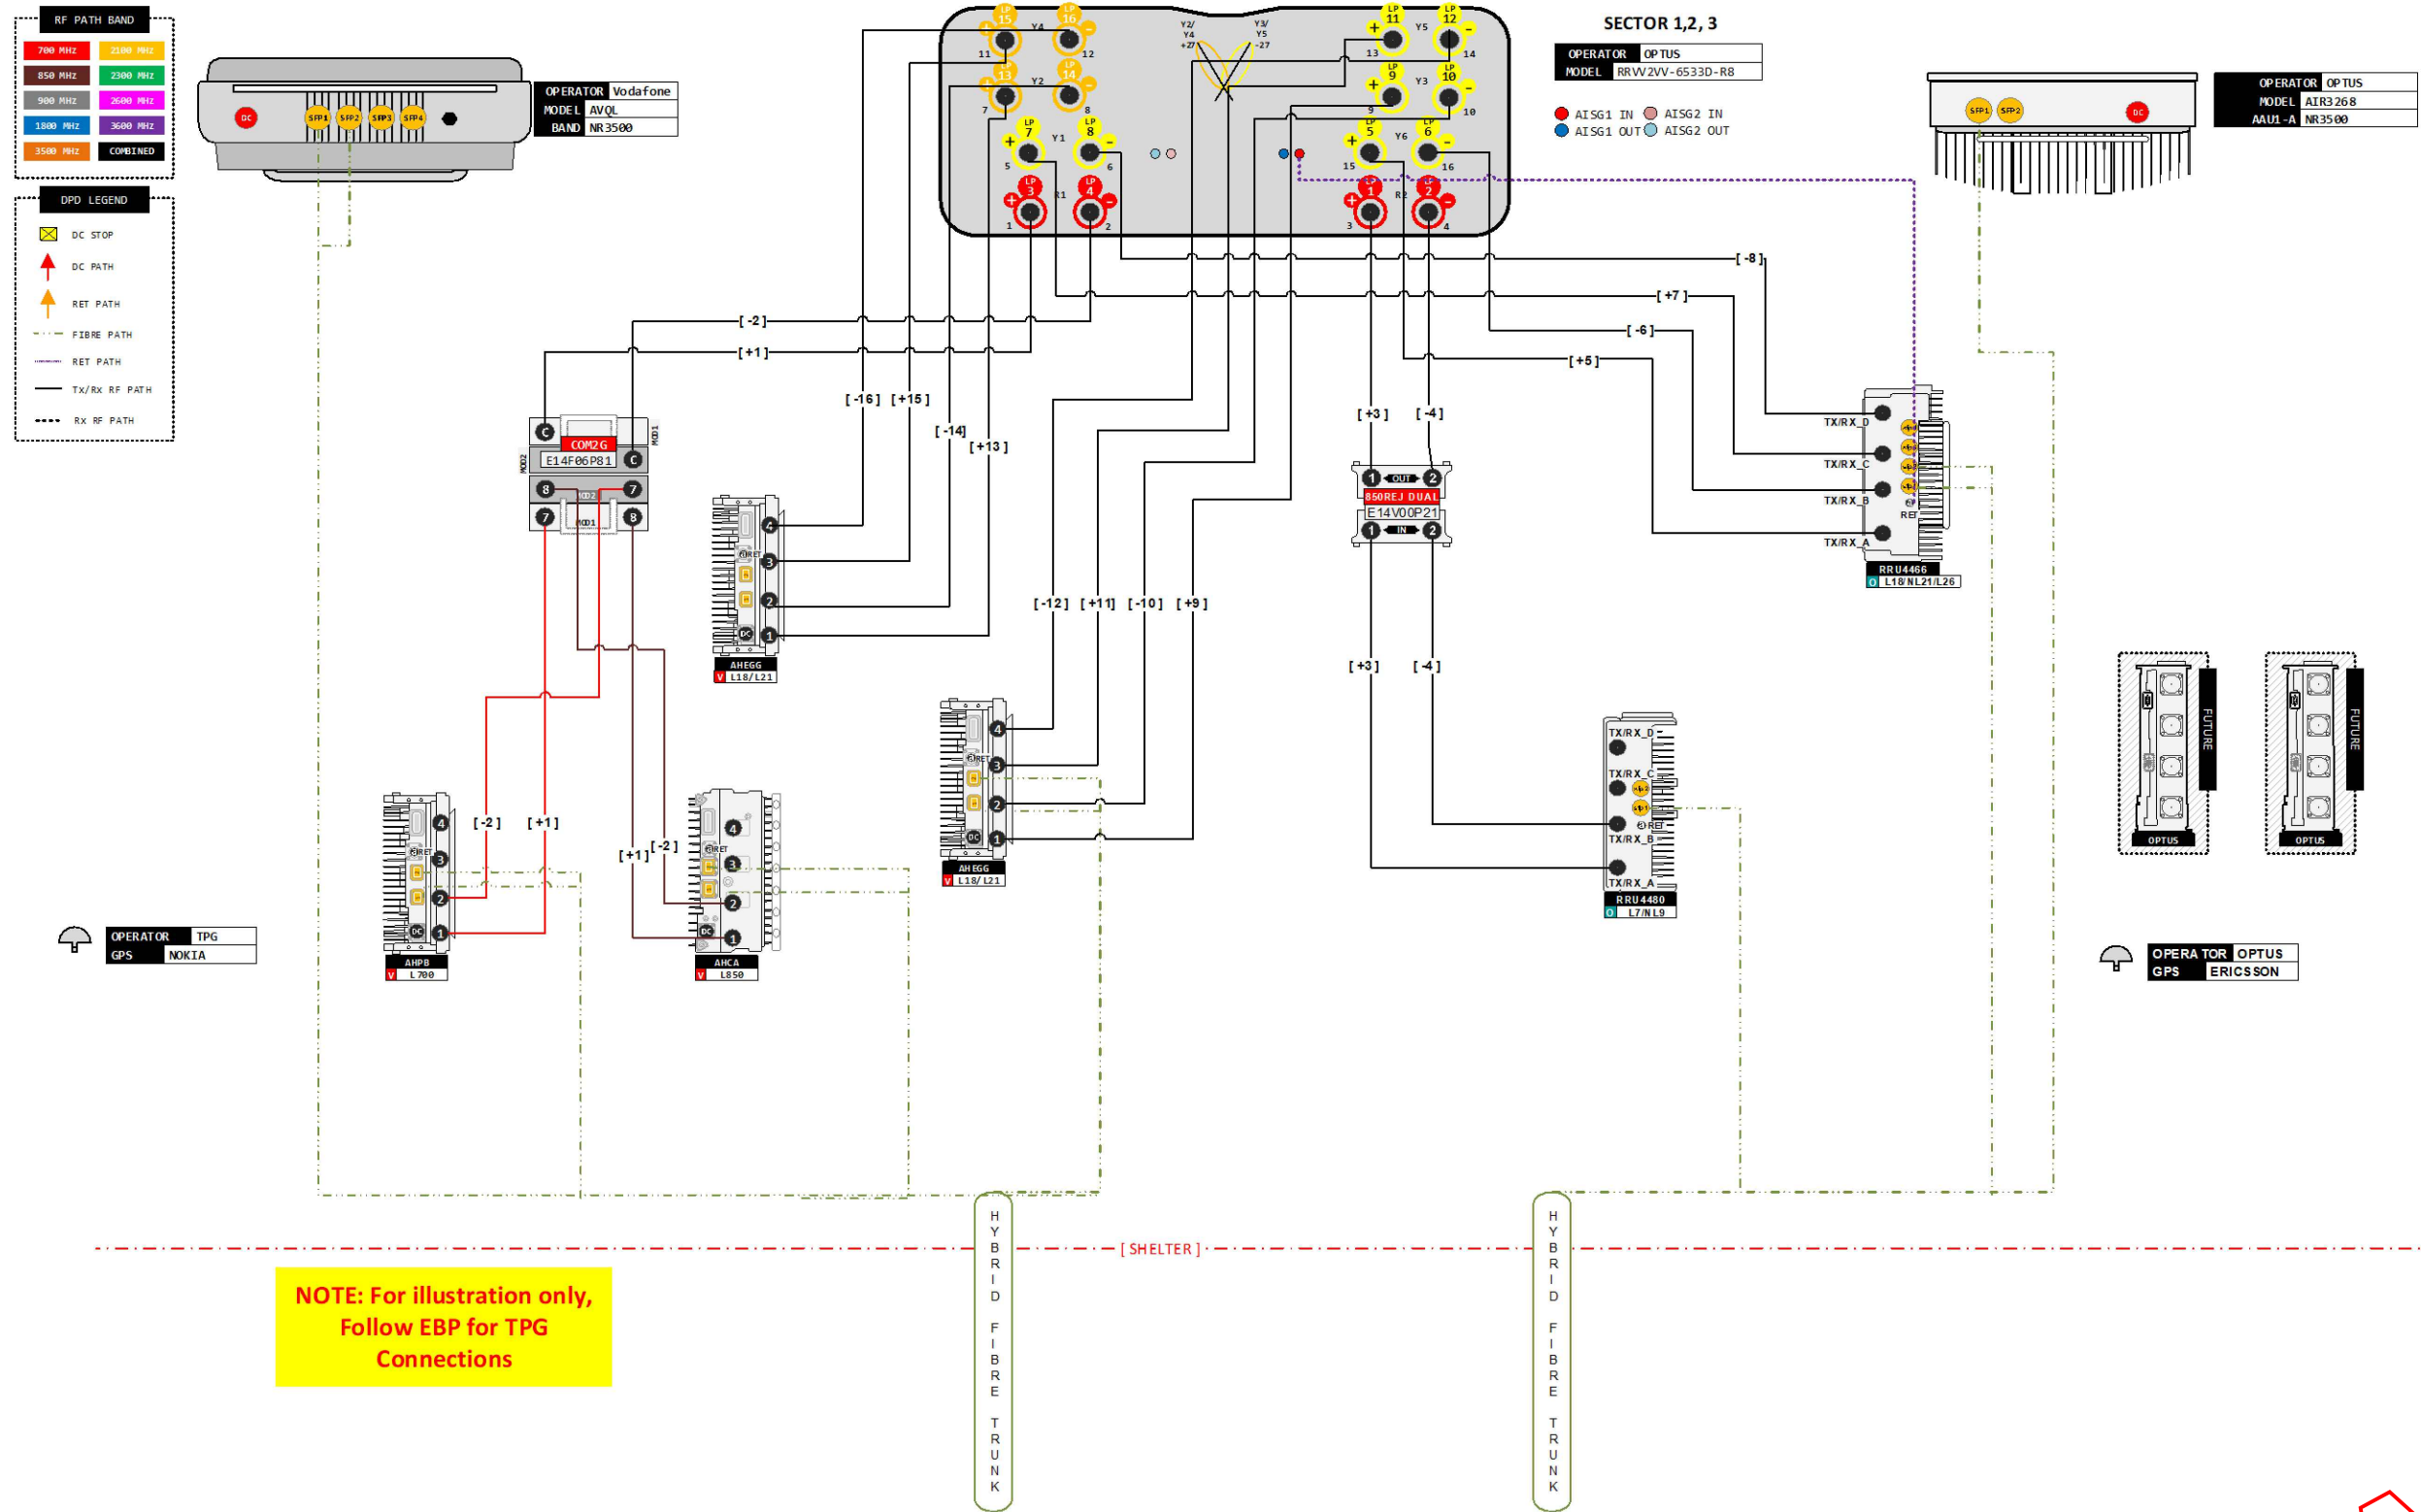

OPTUS & VODAFONE RF PLUMBING DIAGRAM
PER SECTOR

NOTE:

- THIS DRAWING SHALL BE READ IN CONJUNCTION WITH DRAWING H8097-A1, A2 & A3.

Rev	Date	Revision Details	Consultant	CAD	Designer	Verifier	Approver
A	21.10.25	ISSUED FOR CONSTRUCTION (UPGRADE 5G (eJV))	ALL TELECOMS	VB	SA	GL	JM



Client:

Project:

MOBILE NETWORK AUSTRALIA
SITE No:- H8097
AUSTINS FERRY
2 PLAN 158154 WAKEHURST ROAD

Drawing Title:

OPTUS & VODAFONE RF PLUMBING
DIAGRAM

Drawing Status:

FOR CONSTRUCTION

Drawing No.

H8097-P1

Revision

A

