



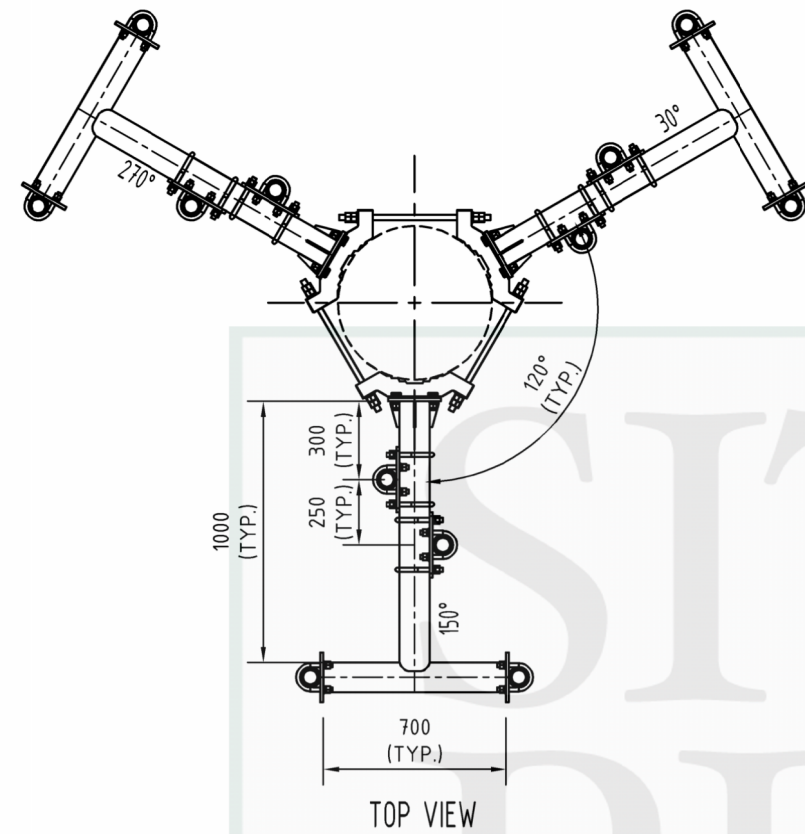

TOP VIEW

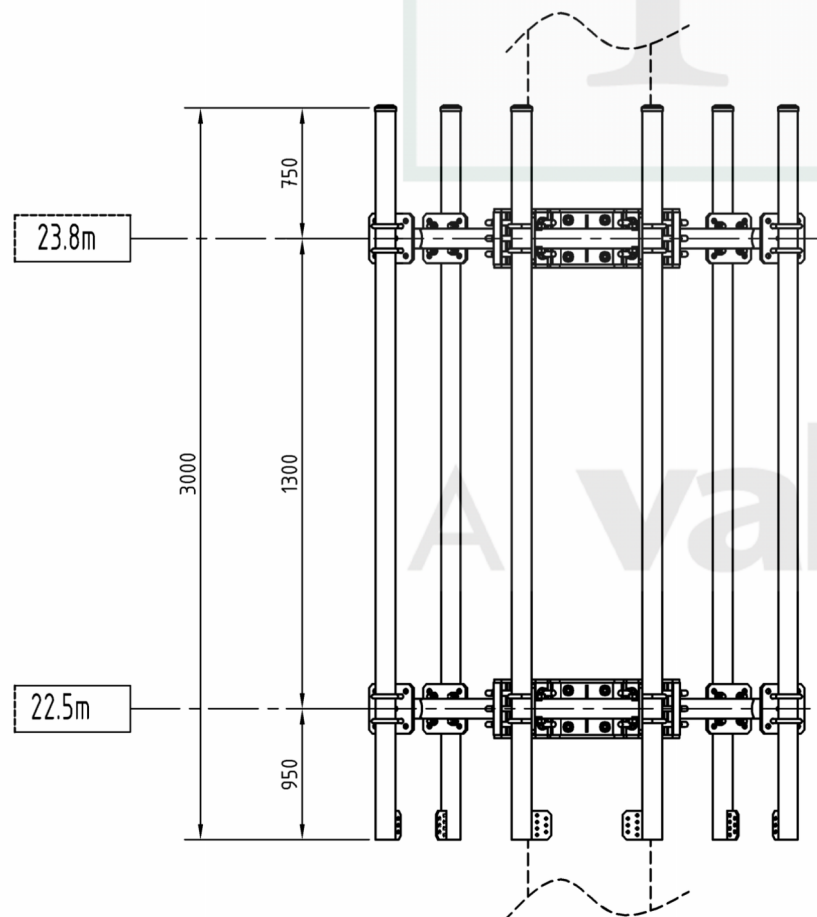

FRONT VIEW

THE HEADFRAME CAN BE ATTACHED TO THE STRUCTURE UTILISING THE STANDARD BRACKET




BRACKET EXAMPLE

VERTICAL PIPE TYPE	PIPE TOP CANTILEVER(mm)	PIPE BOTTOM CANTILEVER(mm)	TOTAL PIPE LENGTH(mm)
4G PIPE ON SECTOR 1,2,3	750	1300	950
5G PIPE ON SECTOR 1,2,3	750	1300	950
RRU PIPE ON SECTOR 1,2,3	750	1300	950


NOTES:

1. DRAWING IS NOT TO SCALE.
2. ELEVATIONS ARE PRESENTED DIAGRAMMATICALLY AND NOT IN TRUE PROJECTIONS.
3. FOR HEADFRAME CONNECTION TO THE POLE REFER TO SHEET 03 HEADFRAME ORDER SHEETS ITEM NO. 1.
4. DIMENSIONS SHOULD NOT BE OBTAINED BY SCALING THE DRAWINGS.
5. ANY SETTING OUT DIMENSIONS ON THE DRAWING SHOULD BE VERIFIED BY THE INSTALLER.
6. SITE PRO 1 HAS ACTED IN GOOD FAITH BASED ON THE PRESENTED INFORMATION. SITE PRO 1 IS NOT RESPONSIBLE FOR THE POLE DIAMETER DIMENSIONS AND ANY UNKNOWN CLASH POINT ON THE POLE. HEADFRAME DESIGN BY SITE PRO 1 IS BASED ON THE MONOPOLE INFORMATION PROVIDED BY OTHERS.


SITE PRO 1 FOR THE PURCHASE OF THIS STEEL WORK AND CERTIFICATION PLEASE CONTACT US ON: 1300 SITEPRO (1300 748 377) sales@sitepro1.com.au www.sitepro1.com.au	PRODUCT NUMBER SP1-1000-700TA0-SP20132		DRAWING NUMBER SP20132-H8097	
	OPTUS SITE NO. H8097 SITE NAME: AUSTINS FERRY-TAS 700mm FACE WIDTH 1000mm OUTRIGGER HEADFRAME			
A valmont COMPANY COPYRIGHT THIS DOCUMENT PRODUCED BY SITE PRO 1 MUST NOT BE COPIED, TRACED, REPRODUCED, OR LENT WITHOUT CONSENT	 NTS DIMENSIONS IN MILLIMETERS	A3		SHEET NUMBER SHEET 01 OF 03
		REV 0 14/10/2025 ISSUED FOR CONSTRUCTION BY JL SS CHD		DRAWN BY: JJ
				CAD FILE No.

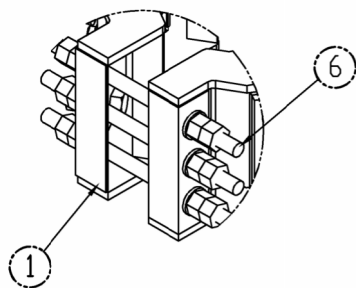


DETAIL B
SCALE 1 : 10
BRACKET EXAMPLE

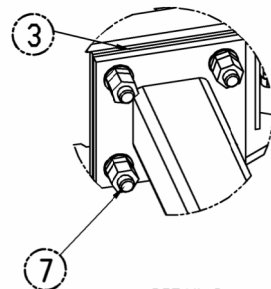



DETAIL B
SCALE 1 : 10
BRACKET EXAMPLE

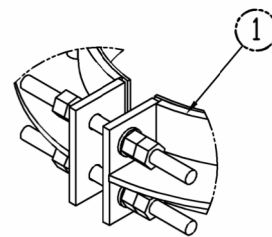

DETAIL B
SCALE 1 : 10
COLLAR EXAMPLE

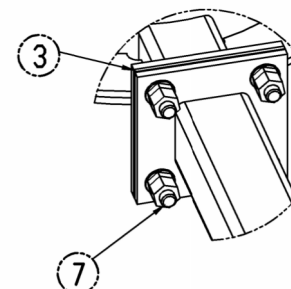

DETAIL B
SCALE 1 : 10
COLLAR EXAMPLE

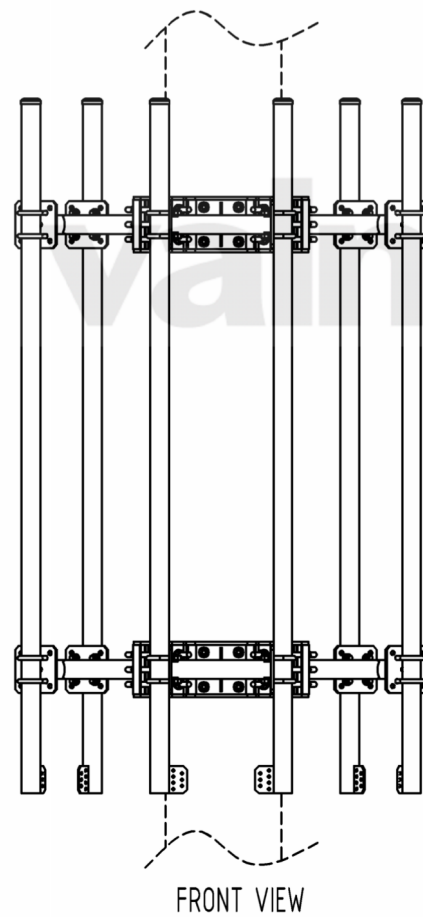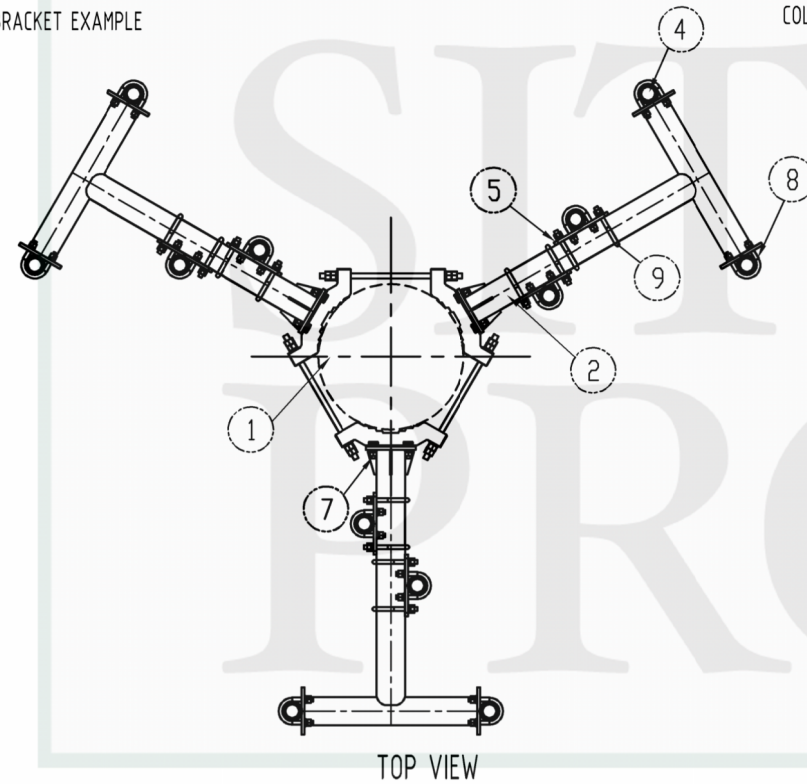


ITEM NO.	PART NAME	DESCRIPTION
STANDARD PARTS		
1	COLLAR/BACKET	STANDARD COLLAR / STANDARD BRACKET
2	T-ARM	TA01000-700
3	PACKER PLATE	PACKER PLATE FOR TOP CONNECTION
4	VERTICAL POST	760D OR 1140D MOUNTING PIPE WITH PRESS-ON-CAP
5	STANDOFF/PLATE	STANDOOFS AS NEEDED/TRANSITION PLATE
HARDWARE		
6	THREADED BARS	M20 THREADED BAR (GRADE 8.8/S) c/w 4N2W
7	CONNECTION BOLT	M20 (x70 LONG) STRUCTURAL BOLT (GRADE 8.8/TB) c/w 1LN1N1W
8	U-BOLT	M16 U-BOLT TO SUIT 76 OD PIPE c/w 2N2LN2W
9	U-BOLT	M16 U-BOLT TO SUIT 114 OD PIPE c/w 2N2LN2W

- NOTES:
- THIS SHEET IS STANDARD DRAWING AND JUST SHOWING THE STANDARD ITEMS DESCRIPTION AND INSTALLATION. FOR SITE SPECIFIC ARRANGEMENT OF HEADFRAME REFER TO SHEET 01.
 - FOR PART DETAILS REFER TO SHEET 03.
 - ITEM 3 (PACKER PLATE) IN UPPER T-ARM CONNECTION IS FOR COMPENSATING THE TAPER IN THE MONOPOLE

BOLTING INSTALLATION PROCEDURE:

- ALL U-BOLTS AND BOLTS DESIGNATED WITH THE NOTATION "/S" ARE TO BE SNUG TIGHTENED AS PER AS/NZS 5131.
- ALL BOLTS DESIGNATED WITH THE NOTATION "TB" ARE TO BE FULLY TENSIONED TO AS/NZS 5131 AS A BEARING JOINT USING THE PART TURN METHOD.

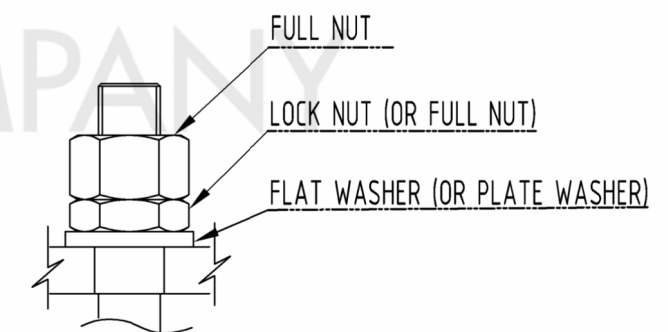

LOCK NUT INSTALLATION METHOD

SITE PRO 1 A valmont COMPANY	FOR THE PURCHASE OF THIS STEEL WORK AND CERTIFICATION PLEASE CONTACT US ON: 1300 SITEPRO (1300 748 377) sales@sitepro1.com.au www.sitepro1.com.au	PRODUCT NUMBER SP1-1000-700TA0-SP20132		DRAWING NUMBER SP20132-H8097					
		OPTUS SITE NO. H8097 SITE NAME: AUSTINS FERRY-TAS 700mm FACE WIDTH 1000mm OUTRIGGER HEADFRAME				SHEET NUMBER SHEET 02 OF 03			
						DRAWN BY: JJ			
COPYRIGHT THIS DOCUMENT PRODUCED BY SITE PRO 1 MUST NOT BE COPIED, TRACED, REPRODUCED, OR LENT WITHOUT CONSENT	 NTS DIMENSIONS IN MILLIMETERS	A3							
		0	14/10/2025	ISSUED FOR CONSTRUCTION	JL	SS	CAD FILE No.		
		REV	DATE	DESCRIPTION	BY	CHKD			

HEADFRAME ORDER SHEET

ITEM NO.	PART NAME	PART NUMBER	DESCRIPTION	MASS (kg)	QUANTITY	TOTAL MASS (kg)
SP1-STANDARD PARTS						
1	BRACKET	SP1-BKTD411	BRACKET TO SUIT Ø400 TO Ø1100 POLES	20.88	6	125.28
				-	-	-
		SRNE010	10mm THICK NEOPRENE RUBBER	-	-	-
	COLLAR AS PER GA60123			-	-	-
				-	-	-
2	T-ARM	TA01000-700	T-ARM OUTRIGGER 1000mm LONG WITH 700mm ARM	38.58	6	231.48
3	PACKER PLATE	OT10PKPL	10mm PACKER PLATE	3.17	3	9.51
		OT20PKPL	20mm PACKER PLATE	6.35	-	-
4	VERTICAL POST	P7625E	2500mm LONG 76 OD ANTENNA MOUNTING PIPE WITH PRESS-ON-CAP	21.31	-	-
		P7628E	2800mm LONG 76 OD ANTENNA MOUNTING PIPE WITH PRESS-ON-CAP	23.81	-	-
		P7630E	3000mm LONG 76 OD ANTENNA MOUNTING PIPE WITH PRESS-ON-CAP	25.48	12	305.76
		P7632E	3200mm LONG 76 OD ANTENNA MOUNTING PIPE WITH PRESS-ON-CAP	34.78	-	-
		P7635E	3500mm LONG 76 OD ANTENNA MOUNTING PIPE WITH PRESS-ON-CAP	38.00	-	-
		P7638E	3800mm LONG 76 OD ANTENNA MOUNTING PIPE WITH PRESS-ON-CAP	41.22	-	-
		P11428E	2800mm LONG 114 OD ANTENNA MOUNTING PIPE WITH PRESS-ON-CAP	36.48	-	-
		P11430E	3000mm LONG 114 OD ANTENNA MOUNTING PIPE WITH PRESS-ON-CAP	39.04	-	-
		P11435E	3500mm LONG 114 OD ANTENNA MOUNTING PIPE WITH PRESS-ON-CAP	45.44	-	-
5	STANDOFF	SP1-ST16100	100mm LONG STANDOFF	8.25	-	-
		SP1-ST16150	150mm LONG STANDOFF	8.79	-	-
		SP1-ST16200	200mm LONG STANDOFF	9.32	-	-
		SP1-ST16250	250mm LONG STANDOFF	9.86	-	-
		SP1-ST16300	300mm LONG STANDOFF WITH STIFFENER	10.94	-	-
		SP1-ST16350	350mm LONG STANDOFF WITH STIFFENER	11.48	-	-
	PLATE	TPL5	TRANSFER PLATE FROM 76 & 114 CHS TO 76 & 114 CHS	8.46	12	101.52
					TOTAL MASS	773.55
HARDWARE						
6	THREADED BAR (FOR BRACKETS ONLY)	TBM20L300	M20 (x300 LONG) THREADED BAR (GRADE 8.8/S) c/w 4N2FW (SUITS Ø250-Ø300	1.25	-	-
		TBM20L500	M20 (x500 LONG) THREADED BAR (GRADE 8.8/S) c/w 4N2FW (SUITS Ø300-Ø500	1.74	-	-
		TBM20L720	M20 (x720 LONG) THREADED BAR (GRADE 8.8/S) c/w 4N2FW (SUITS Ø500-Ø800	2.31	18	41.58
		TBM20L1100	M20 (x1100 LONG) THREADED BAR (GRADE 8.8/S) c/w 4N2FW (SUITS Ø800-Ø1100	3.3	-	-
7	CONNECTION BOLT	SP1-STM20L70	M20 (x70 LONG) STRUCTURAL BOLT (GRADE 8.8/TB) c/w 1LN1N1W	0.45	24	10.8
		SP1-STM20L80	M20 (x80 LONG) STRUCTURAL BOLT (GRADE 8.8/TB) c/w 1LN1N1W	0.52	-	-
		SP1-STM20L90	M20 (x90 LONG) STRUCTURAL BOLT (GRADE 8.8/TB) c/w 1LN1N1W	0.58	-	-
8	U-BOLT	SP1-UB16-76	M16 U-BOLT TO SUIT 76 OD PIPE c/w 2N2LN2W	0.78	48	37.44
9	U-BOLT	SP1-UB16-114	M16 U-BOLT TO SUIT 114 OD PIPE c/w 2N2LN2W	0.96	24	23.04
					TOTAL MASS	112.86

SITE NAME	AUSTINS FERRY
SITE NUMBER	H8097
SAED CONSULTANT	ALL TELECOS
STRUCTURE TYPE	SR3-BM27-585
HEADFRAME HORIZONTAL (FACE) AZIMUTH (°)	30 / 150 / 270
HF TOP & BOTTOM CONNECTION ELEVATION (m)	23.8 TOP 22.5 BOM
POLE DIAMETER AT TOP & BOTTOM CONNECTION (mm)	633 TOP 653 BOM
CERTIFYING COMPANY	SITE PRO 1
INSTALLER COMPANY	
INSTALLATION DATE	

NOTE:

1. IT IS THE DESIGNER RESPONSIBILITY TO ORDER THE CORRECT QUANTITY OF EACH ITEM SPECIALLY IF THEY ARE MAKING ANY CHANGES TO THE ORIGINAL QUANTITY. FOR ANY QUESTION CONTACT SITE PRO 1.
2. ITEM NUMBER 1, 4, 5 & 6 REQUIRE SPECIAL ATTENTION TO ORDER THE CORRECT PART & QUANTITY OF EACH ITEM.
3. IF RUBBERS ARE REQUIRED, PLEASE PLACE THE NUMBER OF RUBBERS REQUIRED FOR THE COLLARS OR BRACKETS ON THE QUANTITY SECTION OTHERWISE PLACE "-" AS QUANTITY. RUBBERS CAN BE UTILISED WHEN ISOLATION OF THE MOUNT FROM THE STRUCTURE IS REQUIRED, OR THE STRUCTURE SURFACE IS ROUGH.

SITE PRO 1 FOR THE PURCHASE OF THIS STEEL WORK AND CERTIFICATION PLEASE CONTACT US ON: 1300 SITEPRO (1300 748 377) sales@sitepro1.com.au www.sitepro1.com.au A valmont COMPANY	PRODUCT NUMBER SP1-1000-700TA0-SP20132		DRAWING NUMBER SP20132-H8097		
	OPTUS SITE NO. H8097 SITE NAME: AUSTINS FERRY-TAS 700mm FACE WIDTH 1000mm OUTRIGGER HEADFRAME				
	DRAWN BY: JJ				
	CAD FILE No.				
COPYRIGHT THIS DOCUMENT PRODUCED BY SITE PRO 1 MUST NOT BE COPIED, TRACED, REPRODUCED, OR LENT WITHOUT CONSENT				NTS DIMENSIONS IN MILLIMETERS	
A3		0 14/10/2025		ISSUED FOR CONSTRUCTION	
REV		DATE		DESCRIPTION	
		BY		CHKD	